



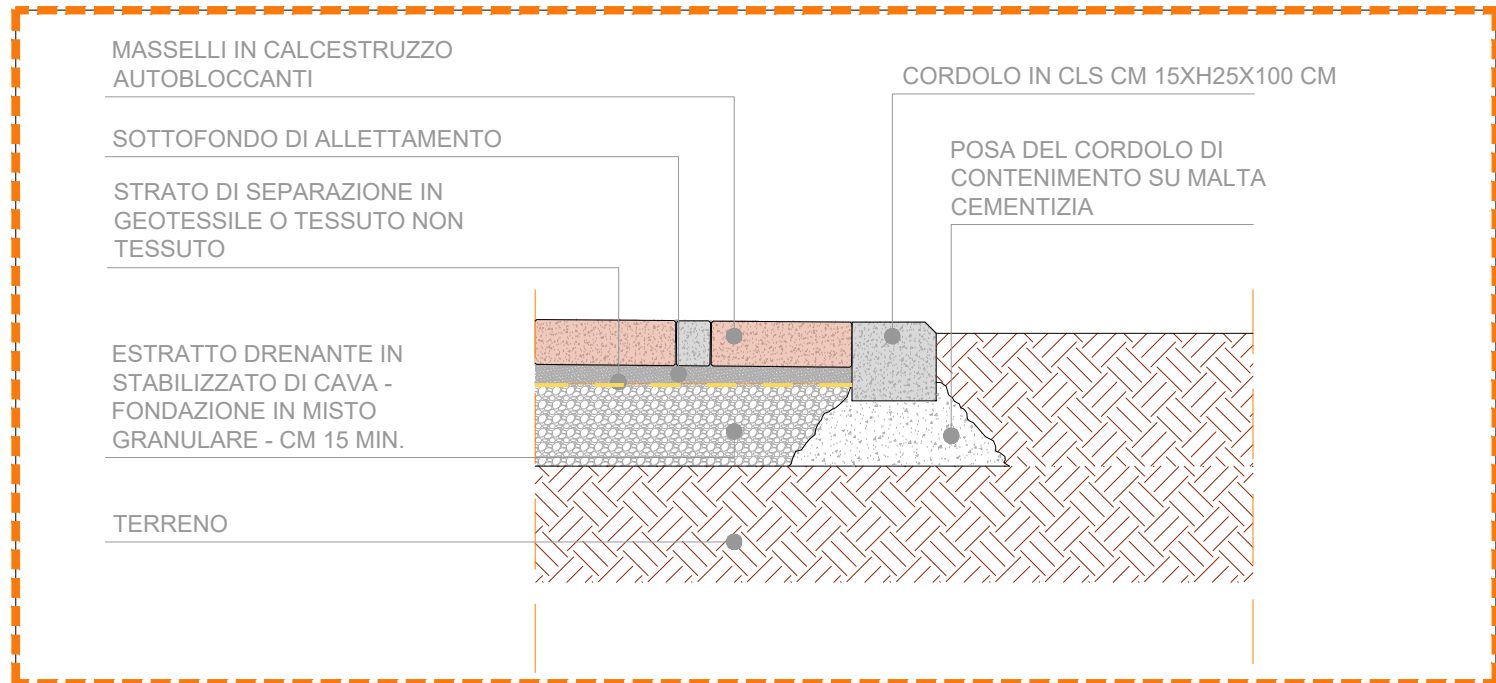

DETTAGLIO 1 - STRATIGRAFIA NUOVA PAVIMENTAZIONE
IN AUTOBLOCCANTI

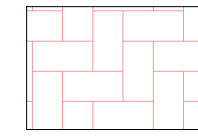

Nuova Pavimentazione realizzata con masselli autobloccanti in calcestruzzo vibro-compresso (tipo FAVARO1, modello Galassia) , con strato di usura avente uno spessore minimo 4 mm. Caratteristiche fisiche meccaniche secondo la norma UNI EN 1338: dimensioni nominali 74x222/148x222/222x222/226x222 mm, spessore nominale 75 mm, tolleranza sullo spessore nominale ± 3 mm, resistenza caratteristica a trazione indiretta per taglio $\geq 3,6$ MPa, carico minimo di rottura per taglio ≥ 250 N/mm, resistenza allo scivolamento/ sdrucciolo soddisfacente. Conforme ai requisiti di antiscivolo di cui al DM 14/06/1989 n.236 per pavimentazioni esterne. Caratteristiche di sostenibilità ambientale: assenza di amianto, contenuto di materiale riciclato secondo CAM EDILIZIA (Decreto del 23-06-2002) $\geq 10,8\%$, indice di riflettanza solare SRI (per materiale grigio e colori a base bianca) secondo ASTM E1980 ≥ 29 . Posta in opera secondo le modalità indicate dalla norma UNI 11241 su massiccata approntata in funzione del tipo di traffico previsto e dello stato del suolo naturale sulla base delle indicazioni del "Catalogo per il dimensionamento delle pavimentazioni in ambito urbano" edito da Assobeton, 2005.

NUOVE PIANTAGIONI

Specie	Q. tà
Fraxinus oxycarpa in zolla circonferenza 18-20	6
Acer campestre in zolla circonferenza 18-20	4
Cercis siliquastrum in zolla circonferenza 18-20	4
Pyrus calleriana "Red Spire" in zolla circonferenza 18-20	4
Prunus cerasifera var pissardi in zolla circonferenza 18-20	4
Prunus serrulata var Kanzan in zolla circonferenza 18-20	2
Tappeto erboso polifita (mq)	1200



 COMUNE DI BAGNO A RIPOLI ISTITUTO DI ISTRUZIONE SUPERIORE "A. VOLTA" PROGETTO ESECUTIVO ai sensi del D.Lgs. 36/2023 LAVORI DI ADEGUAMENTO SISMICO	
 	
COMMITTENTE  CITTÀ METROPOLITANA DI FIRENZE Proprietà: Città Metropolitana di Firenze Responsabile unico del procedimento: Ing. Gianni Paolo Cianchi Direttore dell'esecuzione del contratto: Ing. Matteo Galatro	CUP B37G22000540001
GRUPPO DI PROGETTAZIONE  Diret. Tec. (art. 36 allegato II.12 D. Lgs. 36/2023) Ing. Pietro Bruscoli Ingegneringhi di Firenze n. 3884 HYDEA S.p.A. via del Rosso Fiorentino 2g 50142 Firenze (Italia) Tel. 057 719491 mail@hydea.it https://www.hydea.it/	RESPONSABILE INTEGRAZIONE DELLE PRESTAZIONI SPECIALISTICHE <i>Ing. Pietro Bruscoli</i> ACUSTICA <i>Ing. Stefano Monni</i> COORDINAMENTO DELLA SICUREZZA <i>Arch. Gabriele Rovetini</i>
Hlab ENGINEERING  Hlab ENGINEERING Hlab Engineering S.r.l. Via del Rosso Fiorentino 2g 50142 Firenze (Italia)	PROGETTAZIONE STRUTTURALE <i>Ing. Emiliano Colonna</i>
OPERE EXTRA APPALTO	
ORGANISMO DI ISPEZIONE  ITS CONTROLLI TECNICI SPA ITS Controlli Tecnici S.p.A. Via delle Formiche 44 00165 Roma (Italia) Tel. 06-9817101 https://www.itscontrollitecnici.it	VERIFICA PROGETTO ai sensi dell'Allegato I.7 D. Lgs. 36/2023
CODICE ELABORATO	ISV-PE-EX-PG-GE-01-01
DESCRIZIONE ELABORATO	SISTEMAZIONI ESTERNE - PREFABBRICATO E IMPIANTI
SCALA 1:200	REDATTO <i>Hydea S.p.A.</i> REVISIONE <i>B</i> DATA <i>LUGLIO 2026</i>