

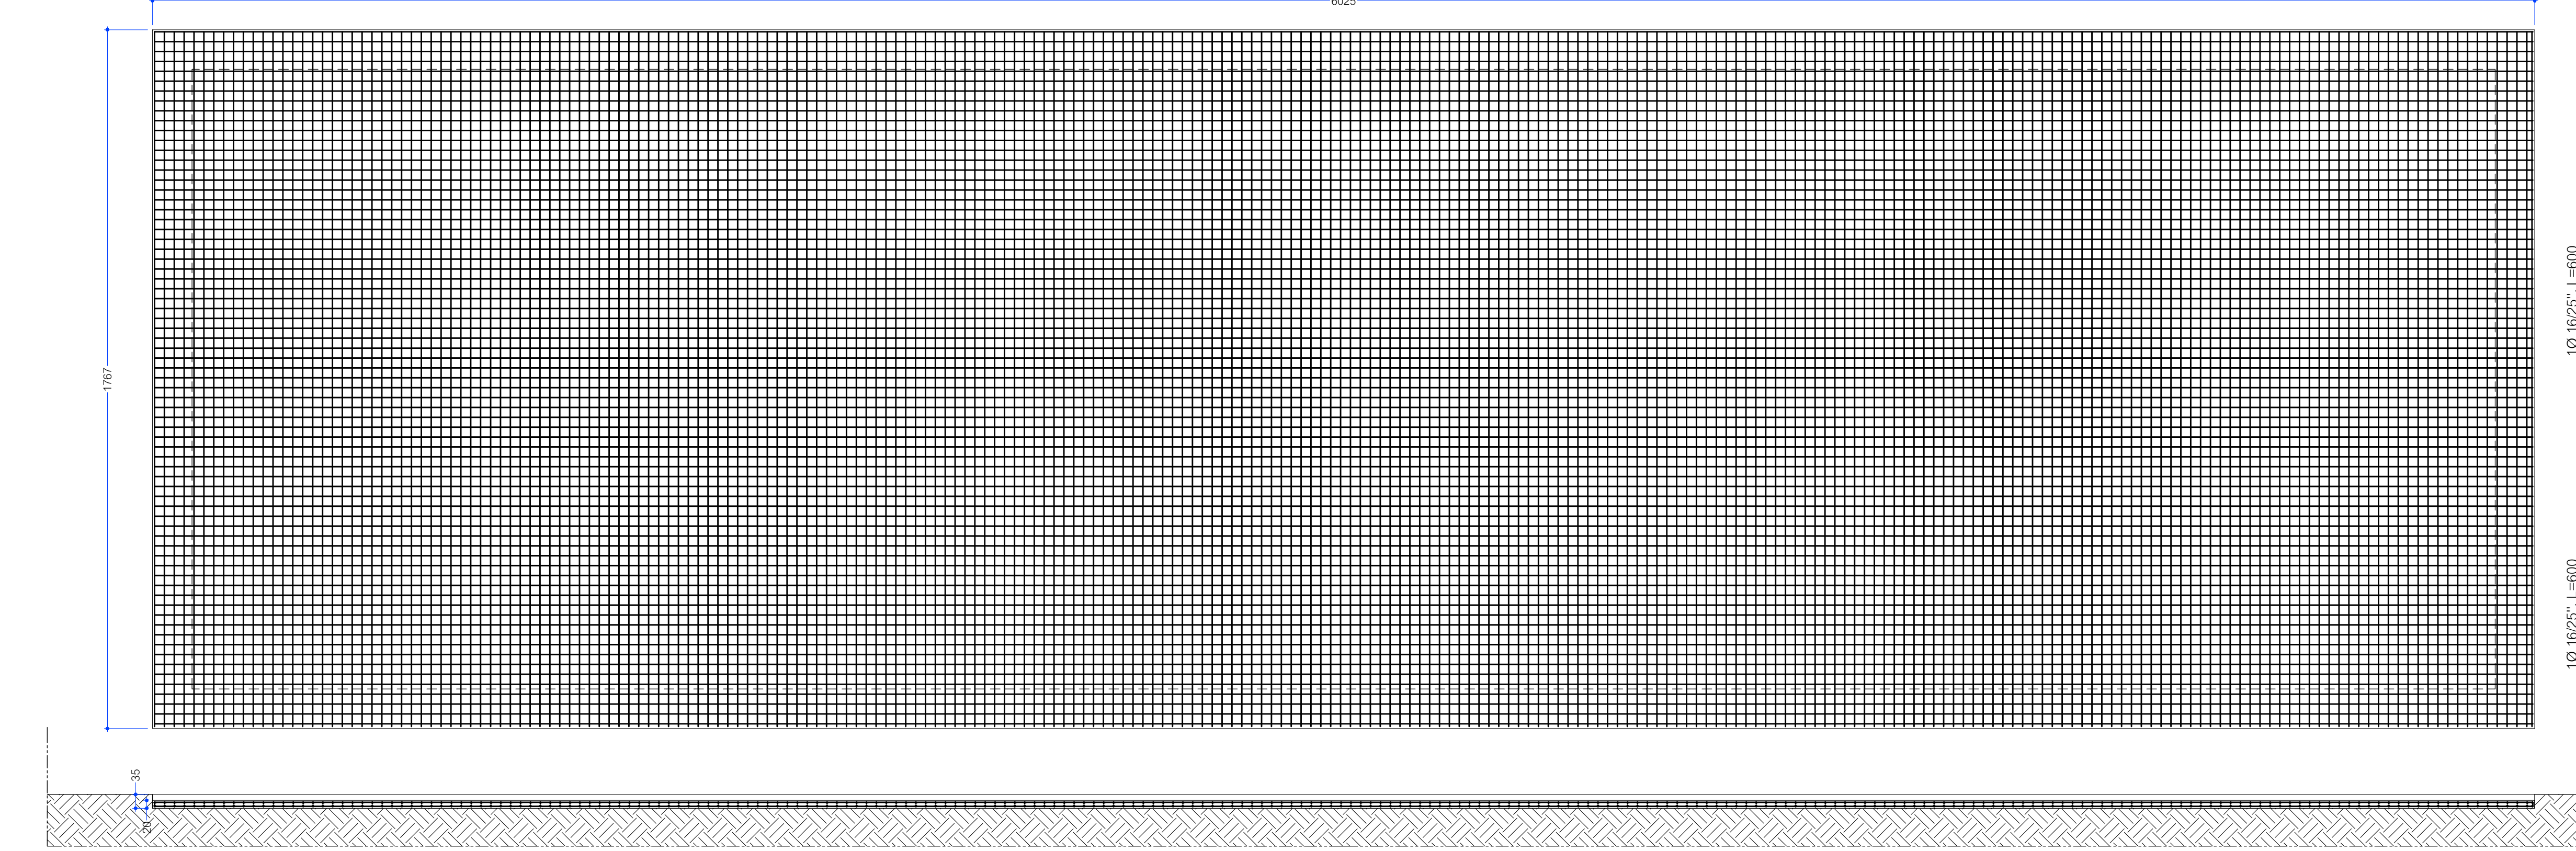
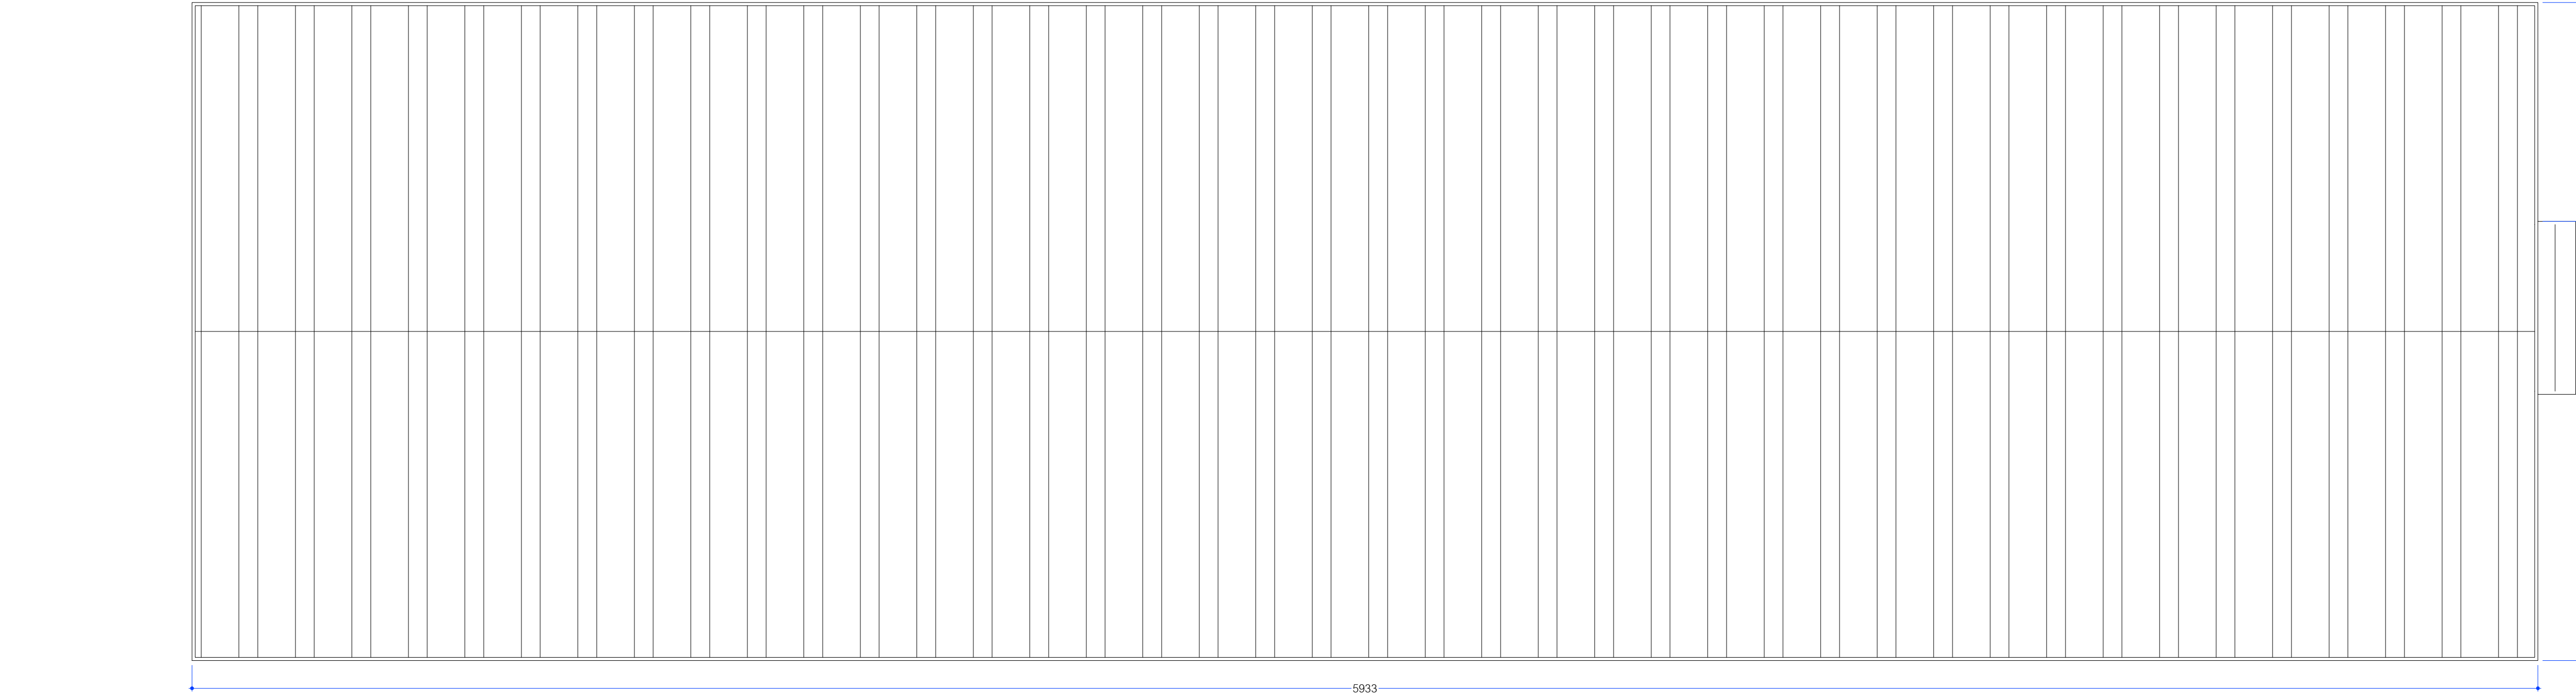
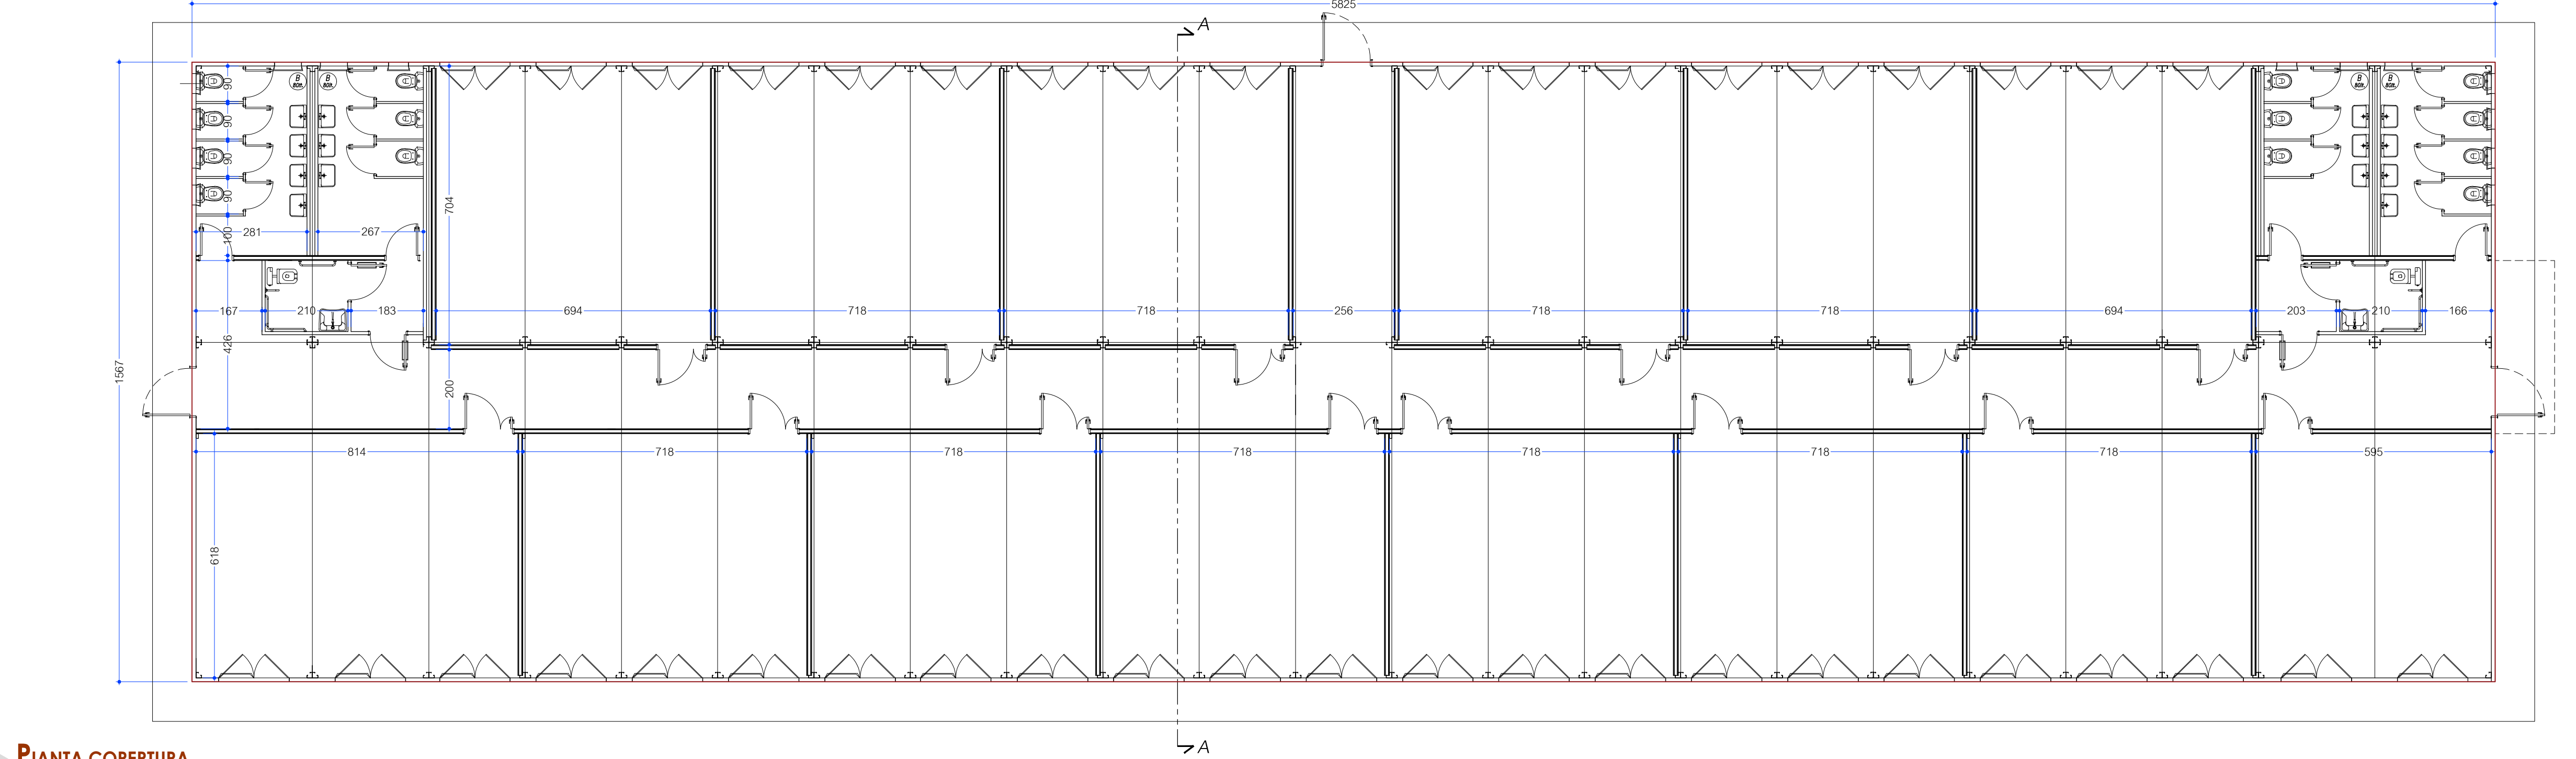
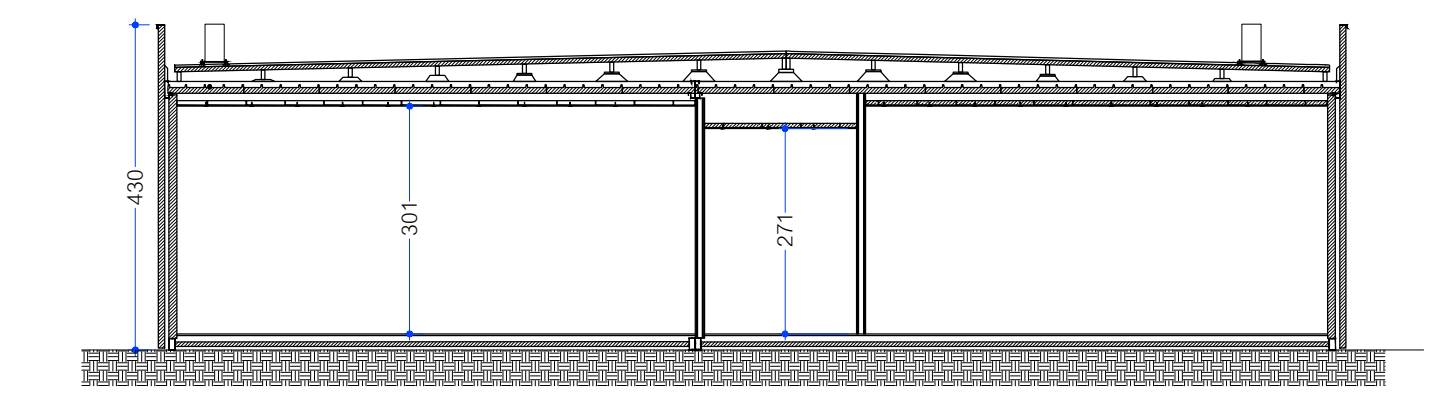
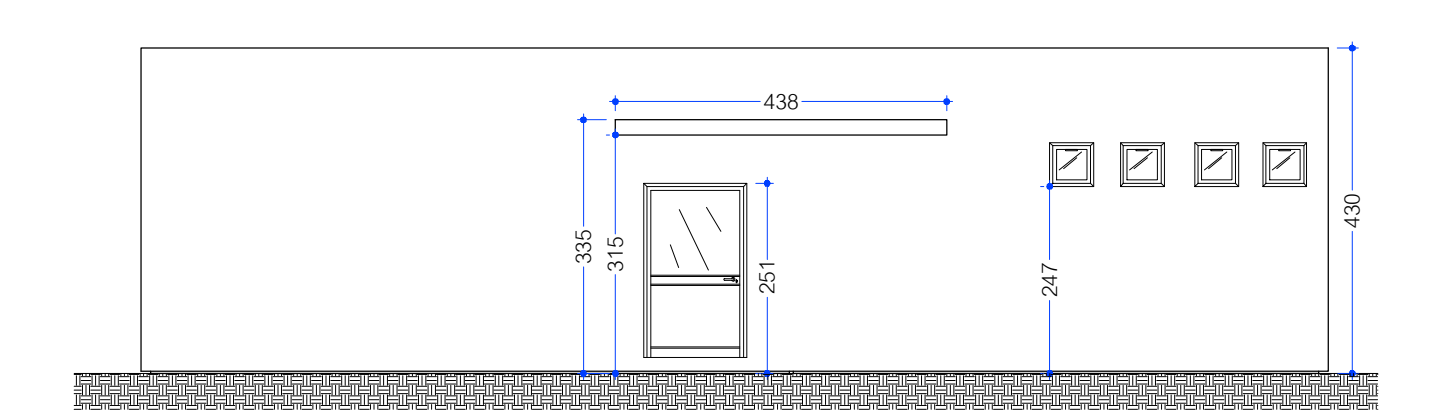
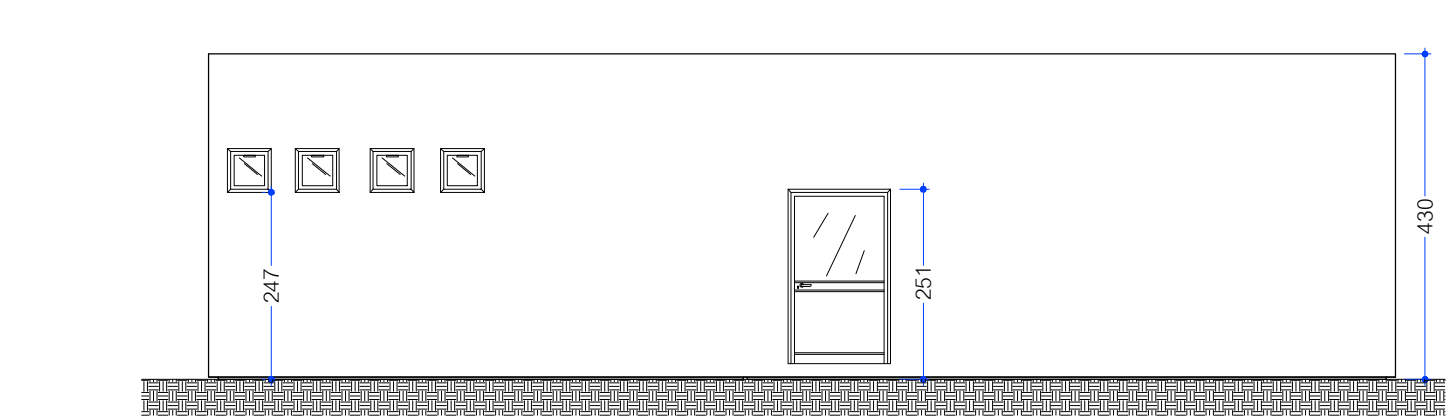


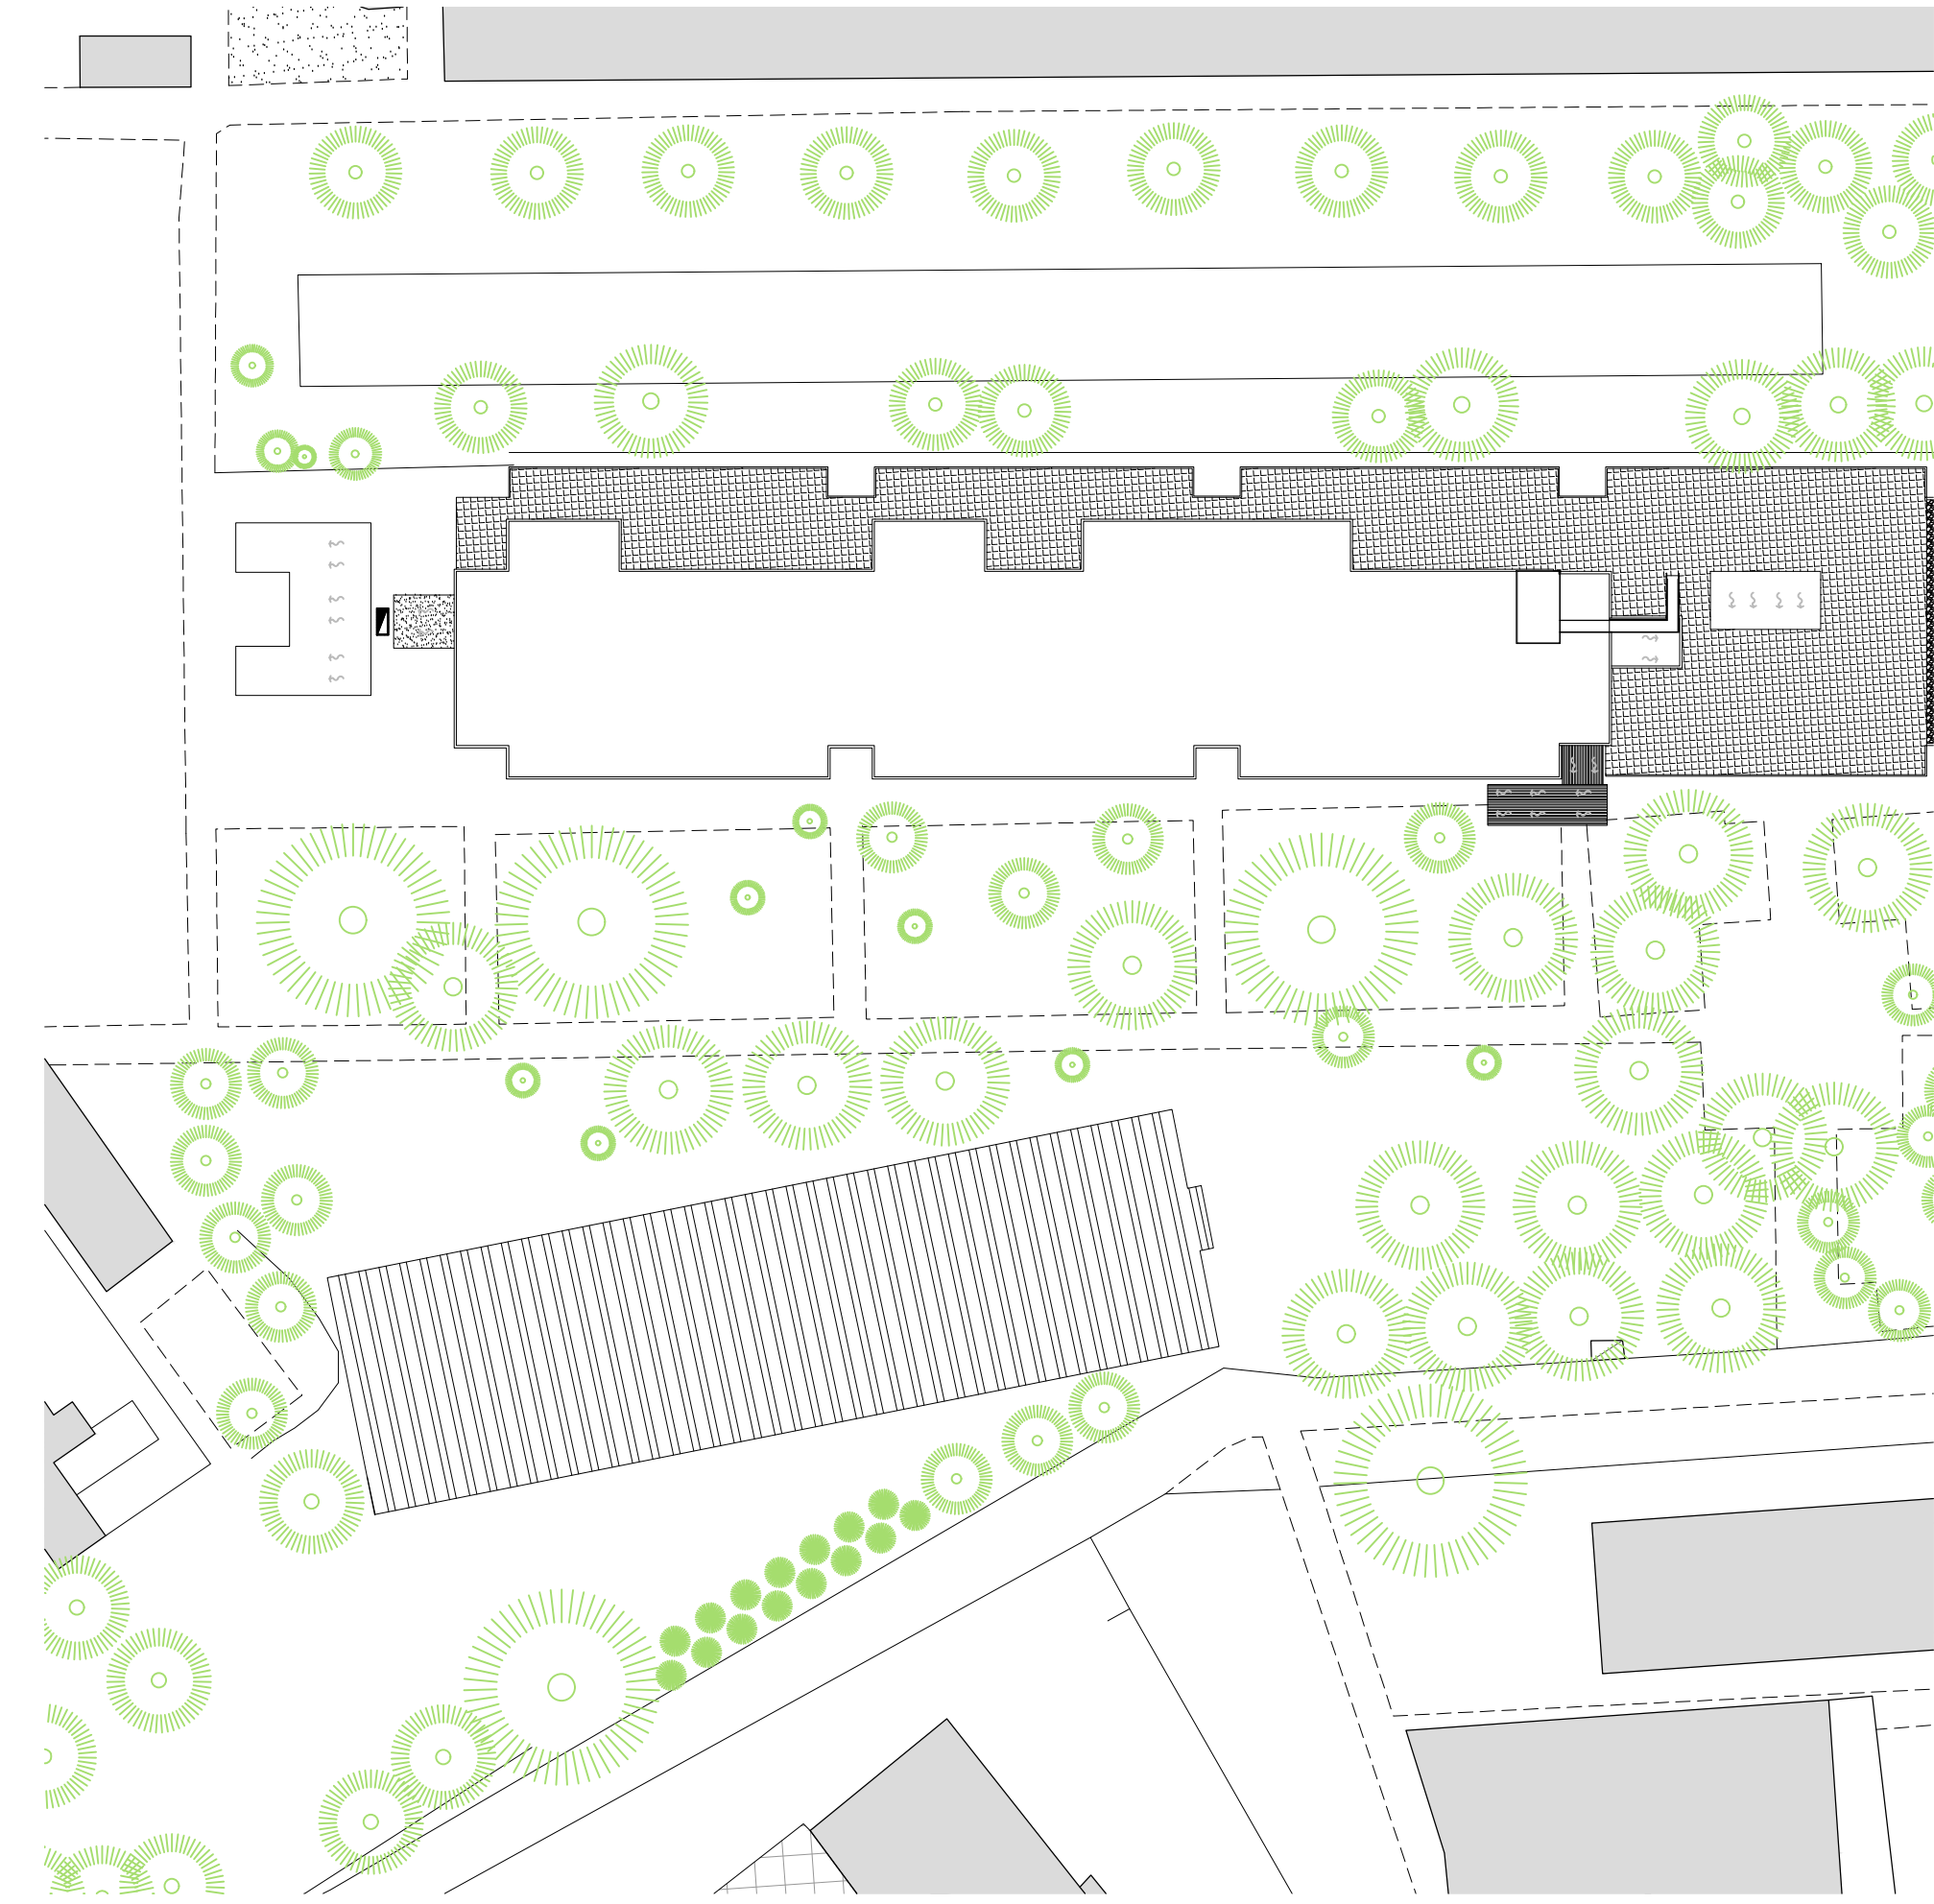


▶ CALCESTRUZZO CAM PER MAGRONE	C13/15 - S3 - Dmax 40mm
▶ CALCESTRUZZO CAM PER FONDAZIONI	C25/30 - S4 - X/2 - Dmax 20mm
▶ CALCESTRUZZO CAM PER ELEVAZIONI	C25/30 - S4 - X/1 - Dmax 20mm
▶ BOLLICIA PER MICROPIALI	Cemento PS35, rapporto a/c = 0,4
▶ ACCIAIO PER CEMENTO ARMATO CAM	B450C controllato in stabilimento
▶ ACCIAIO PER MICROPIALI CAM	S355JR - UNI EN 10025-2
▶ ACCIAIO PER CARPENTERIA METALLICA CAM	S235JR - UNI EN 10025-2
▶ ANCORAGGI CHIMICI	Resina epossidica bicomponente
▶ ANCORAGGI MECCANICI	Tasselli metallici anelati da c.a.
▶ RETE BD/PEZONALE ANTIRIBALTAMENTO	Rete in fibra di vetro approntata
▶ ADESIVO PER ANTIRIBALTAMENTO	Adesivo monocomponente a base di dispersione polimerica all'acqua

- ▶ LE FORATURE PER BALLONI, BARRE FILETTATE E PERNI, SE NON DIVERSAMENTE SPECIFICATO, SI INTENDONO FOR CALIBRATI. LA STAZIONE APPALTANTE, PRIMA ORDINAZIONE DELLE PIASTRE IN ACCIAIO PER LE INCAICATURE, DEVE CONTROLLARE L'EFFETTIVA DIMENSIONE DEGLI ELEMENTI IN C.A. DA RINFORCIARE.
- ▶ PRESCRIZIONI FORATURE PER VITI - ØNOMI: PREFORO GUIDA DEL DIAMETRO E LUNGHEZZA DEL SOLO GAMBO NON FILETTATO DELLA VITE E PREFORO GUIDA PER IL FILETTO PARI AL 70% DEL DIAMETRO DEL GAMBO.
- ▶ CORRIERIERO NETTO DELLE ARMATURE PER STRUTTURE DI FONDAZIONE = 4 cm
- ▶ CORRIERIERO NETTO DELLE ARMATURE PER STRUTTURE IN ELEVAZIONE = 3 cm
- ▶ LA STAFFA DI CONTENIMENTO DEVE ESSERE ASSICURATA ALLE BARRE LONGITUDINALI TRAMITE GANCI A 135° PROLUNGATI PER ALMENO DIECI CENTIMETRI ALLE DUE ESTREMITÀ.
- ▶ PRESCRIZIONI GEOMETRICHE PER LA PIEGATURA DEI FERRI

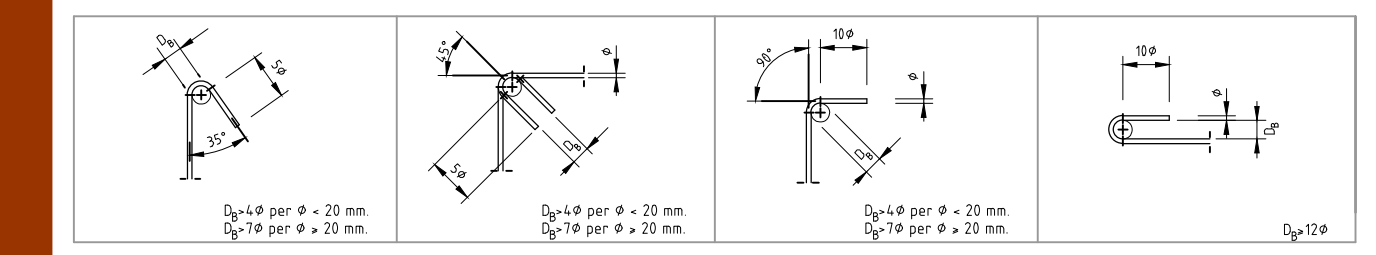

- ▶ TUTTE LE SALDATURE D'ANGOLO AVRANNO SPESSORE "w" UGUALE A 1/2 DELLO SPESSORE "t" MINIMO DA SALDARE.
- ▶ SPECIFICHE PER STRUTTURE METALLICHE AI SENSI DELLA NORMA EN 1090:
 - CLASSE DI ESECUZIONE: EXC3;
 - GRADO DI PREPARAZIONE: P2;
 - CLASSE DI TOLLERANZA: 1 (L=3mm);
 - GRADO DI CORROSIVITÀ: C1;
 - DURATA PREVISTA DELLA PROTEZIONE: > 15 anni.
- ▶ z = altezza saldatura
a = altezza di gola saldatura

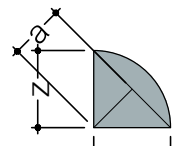

- ▶ INDICAZIONI GENERALI
- ▶ L'APPALTATORE È TENUTO A VERIFICARE, PRIMA DELL'ESECUZIONE DELLE LAVORAZIONI, LA CORRESPONDENZA DELLE DIMENSIONI RAPPRESENTATE NEGLI ELABORATI GRAFICI CON LA SITUAZIONE REALE. QUALORA VENISSERO RISCOPERTE DIFFERENZE SIGNIFICATIVE, TAL DA MODIFICARE SOSTANZIALMENTE LA PROGETTAZIONE ED I PARTICOLARI COSTRUTTIVI, GLI INTERVENTI CONSEGUENTI DOVRANNO ESSERE INDICATI DALLA D.L.
- ▶ LE LAVORAZIONI DI PROGETTO DOVRANNO ESSERE ESEGUITE SOLTANTO DOPO LE ORE 14.00, PER NON APPRECIARE DISTURBO ALLE ADIACENTI STRUTTURE SCOLASTICHE.
- ▶ TUTTE LE DIMENSIONI SONO IN CENTIMETRI, SALVO DOVE DIVERSAMENTE INDICATO.
- ▶ SI PRESCRIVE LA VERIFICA DEL CORRIERIERO DI TUTTE LE TRAM IN C.A. SU CUI SI ANDRÀ AD EFFETTUARE IL RINFORZO, E, SE NECESSARIO, LA STESSA VERIFICA ANDRÀ ESTESA A TUTTI GLI ELEMENTI IN C.A. PER LA DETERMINAZIONE DELLE CARATTERISTICHE REI.

- ▶ Incastellature in acciaio delle travi
- ▶ Nuova soletta in c.a.
- ▶ Demolizione e ricostruzione
- ▶ Micropali
- ▶ Ripristino collegamenti pannelli prefabbricati in c.a. di telai strutturali
- ▶ Incastellature in acciaio pilastri
- ▶ Presidio antiribaltamento tamponature interne
- ▶ Presidio antiribaltamento tamponature esterne

ISTITUTO DI ISTRUZIONE SUPERIORE "A. VOLTA"

PROGETTO ESECUTIVO

LAVORI DI ADEGUAMENTO SISMICO

COMMITTENTE

Proprietà: Città Metropolitana di Firenze

Responsabile unico del procedimento: Ing. Gianni Paolo Cianchi

Responsabile dell'esecuzione del contratto: Ing. Matteo Galassi

B37G200054/0001

GRUPPO DI PROGETTAZIONE

HYDEA S.p.A.

00144 Roma (Italia)

06 5719891

06 5719892

0